


LMR
HANCOCK FARM COMPANY Pty Ltd.
LMR MACADAMIA FARM
MISSINGHAM ROAD
DORROUGHBY

LOCALITY: DUNOON
LGA: LISMORE
CADFILE:LM090092-SV12
CIVILCADFILE:LM090092.C06

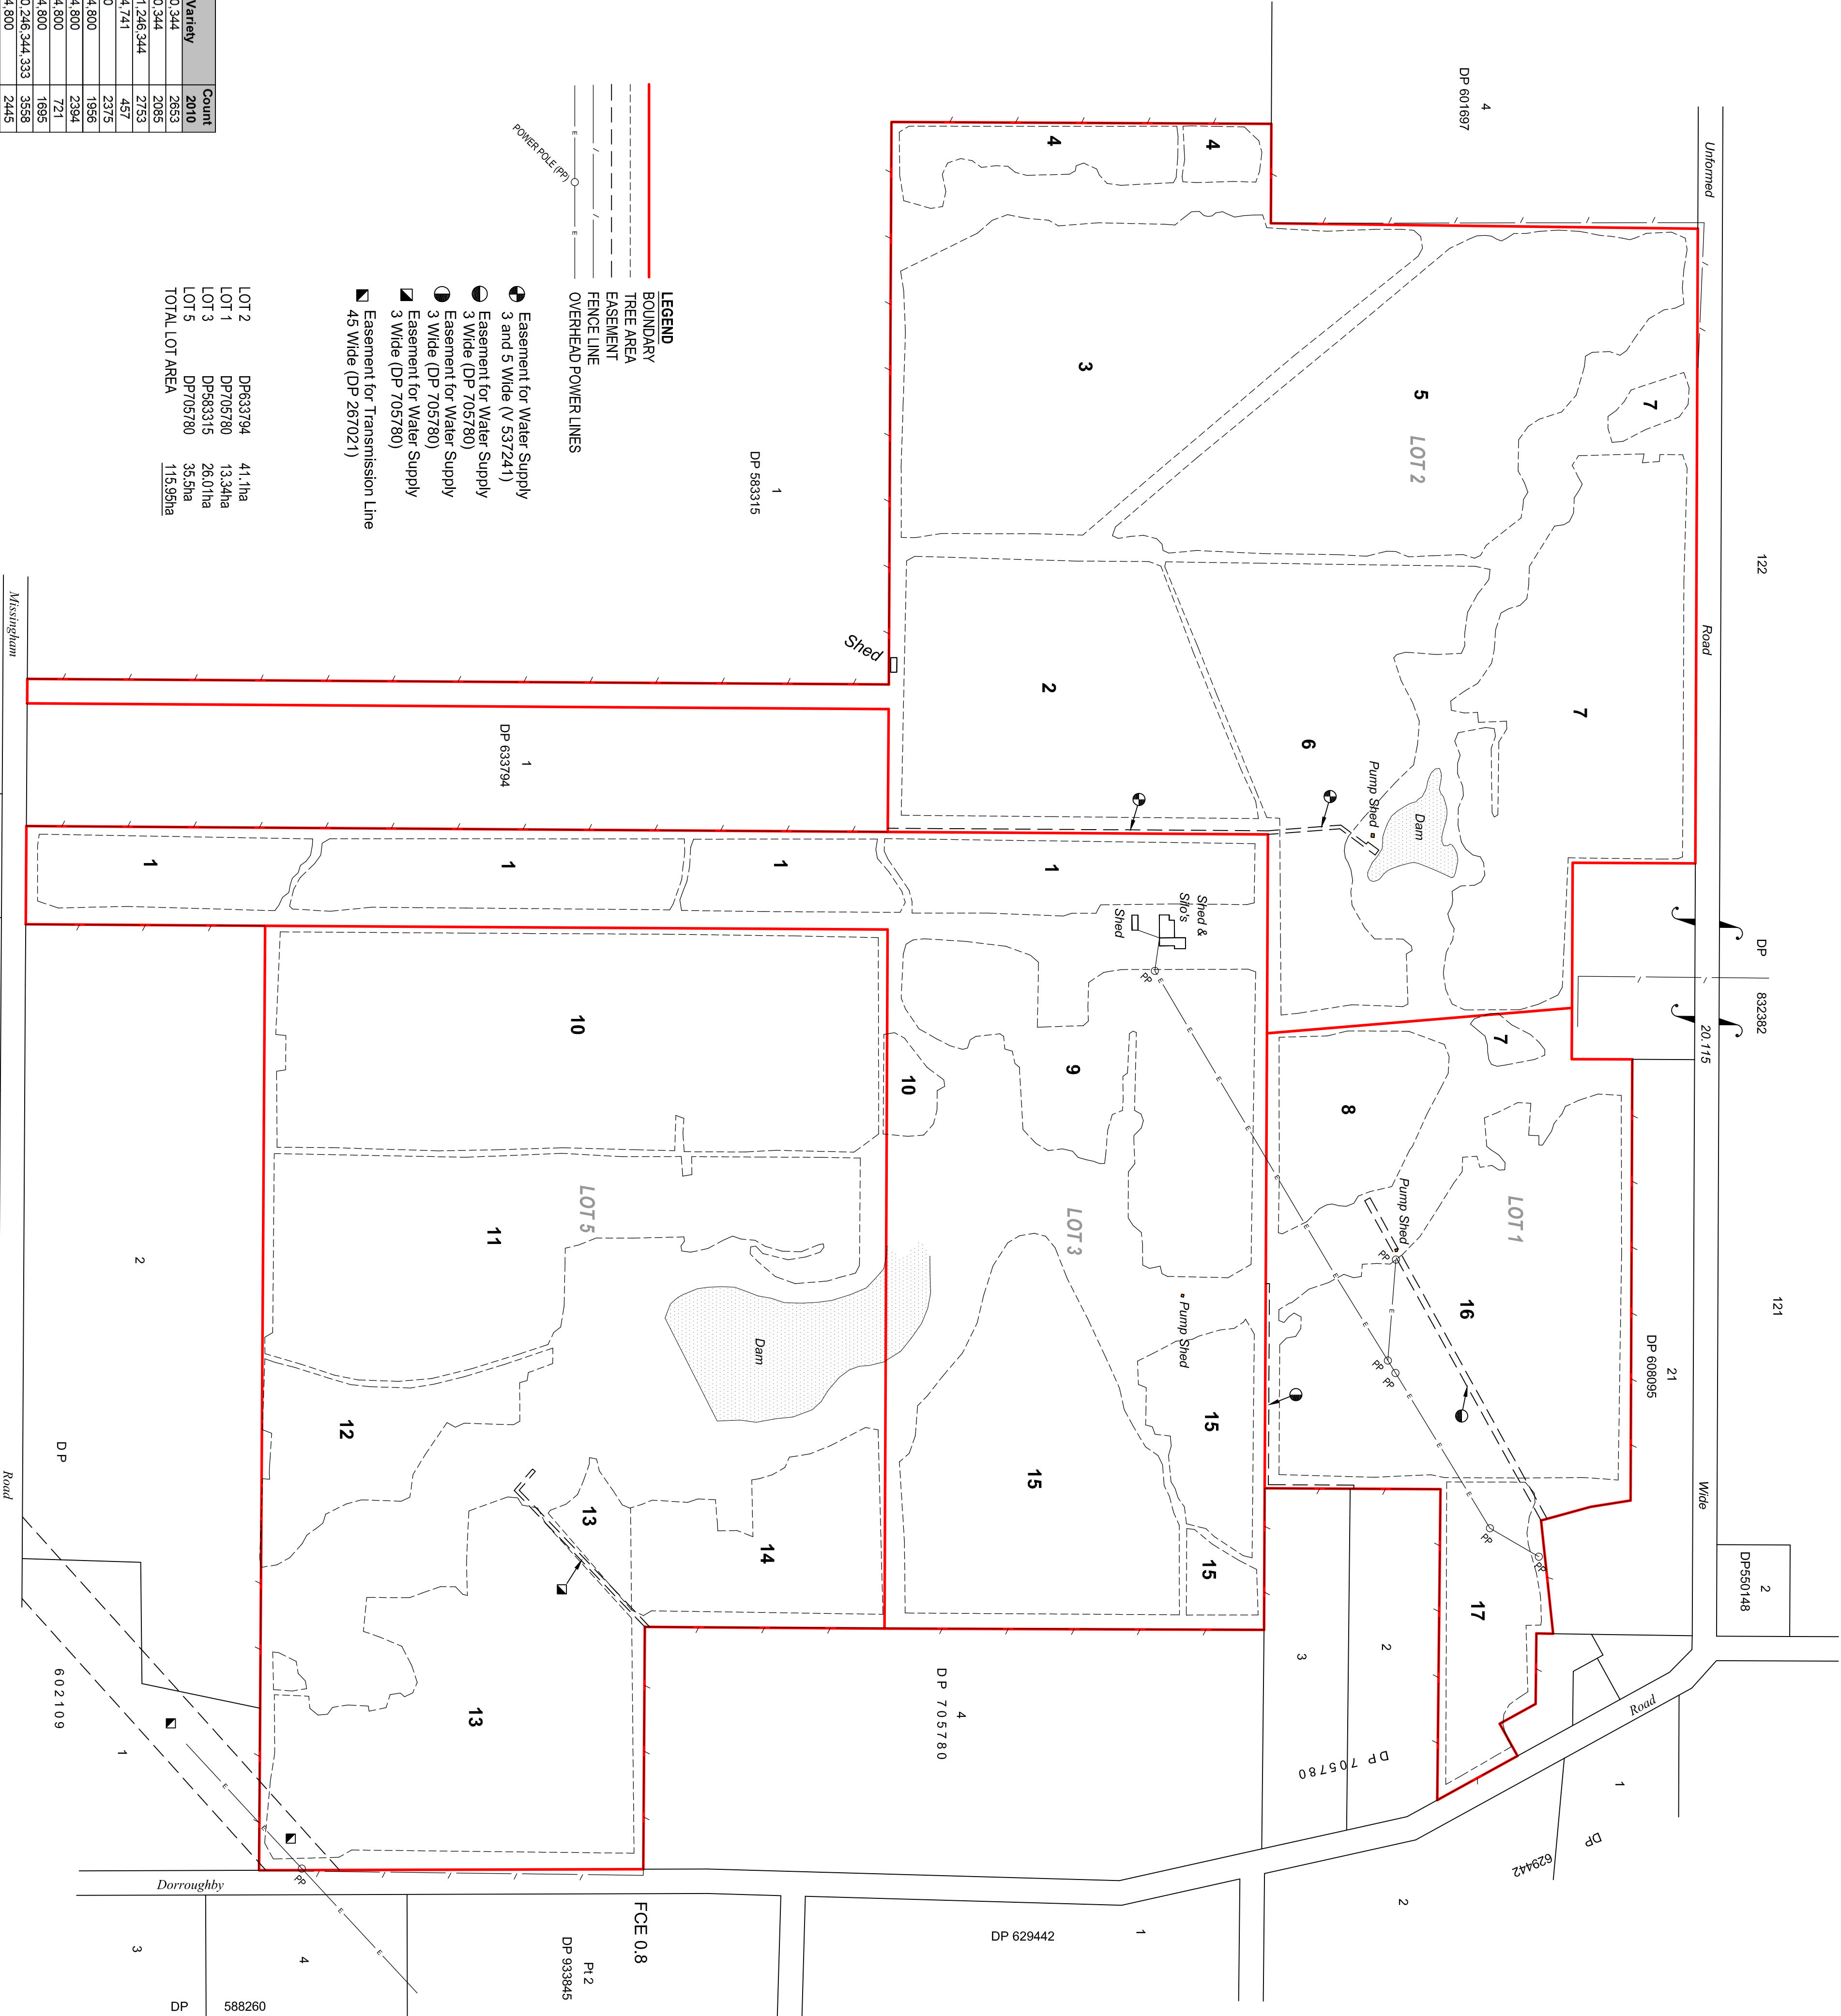

LandPartners Limited

26 Carrington Street, Lismore
NSW 2480, Australia
Phone: (02) 9627 2800, Fax: (02) 9627 1984
www.landpartners.com.au

Surveyed: LM Date Surveyed: JULY2011
Drawn: G.C Checked:

Dwg. No.

LM090092-SV12

Year	Planned	Block	Planted	Tree	Row	Variety	Count
			Area ha	Spacing	Spacing		2010
1989	1		5.63	3.5	7	246 800 344	2653
1987	2		5.27	3.5	7	246 800 344	2065
1983	3		7.46	3.5	7	660 741 246 344	2753
1984	4		1.25	3.5	7	246 344 741	
1990	5		6.58	3.5	7	246 480	2375
1990	6		4.81	3.5	7	246 344 800	1956
1990	7		6.32	3.5	7	246 344 800	2394
1991	8		1.67	3.5	7	246 344 800	721
1990	9		4.26	3.5	7	246 344 800	1695
1989	10		8.97	3.5	7	508 800 246 344 333	3558
1985	11		6.04	3.5	7	246 344 800	1695
1988	12		1.88	3.5	7	246 344 800	725
1990	13		6.47	3.5	7	246 344 800	2507
1991	14		2.22	3.5	7	246 344 800	1051
1988	15		6.53	3.5	7	246 344 800	2657
1990	16		6.47	3.5	7	246 344 800	2657
1990	17		1.52	3.5	7	246 344 800	602
Total			83.34				33271

LOT 2 DP633794 41.1ha
LOT 1 DP705780 13.34ha
LOT 3 DP583315 26.01ha
LOT 5 DP705780 35.51ha
TOTAL LOT AREA 115.95ha

- Easement for Water Supply 3 and 5 Wide (V 537241)
 Easement for Water Supply 3 Wide (DP 705780)
 Easement for Water Supply 3 Wide (DP 705780)
 Easement for Water Supply 3 Wide (DP 705780)
 Easement for Transmission Line 45 Wide (DP 267021)

- LEGEND**
 BOUNDARY
 TREE AREA
 EASEMENT
 FENCE LINE
 OVERHEAD POWER LINES