


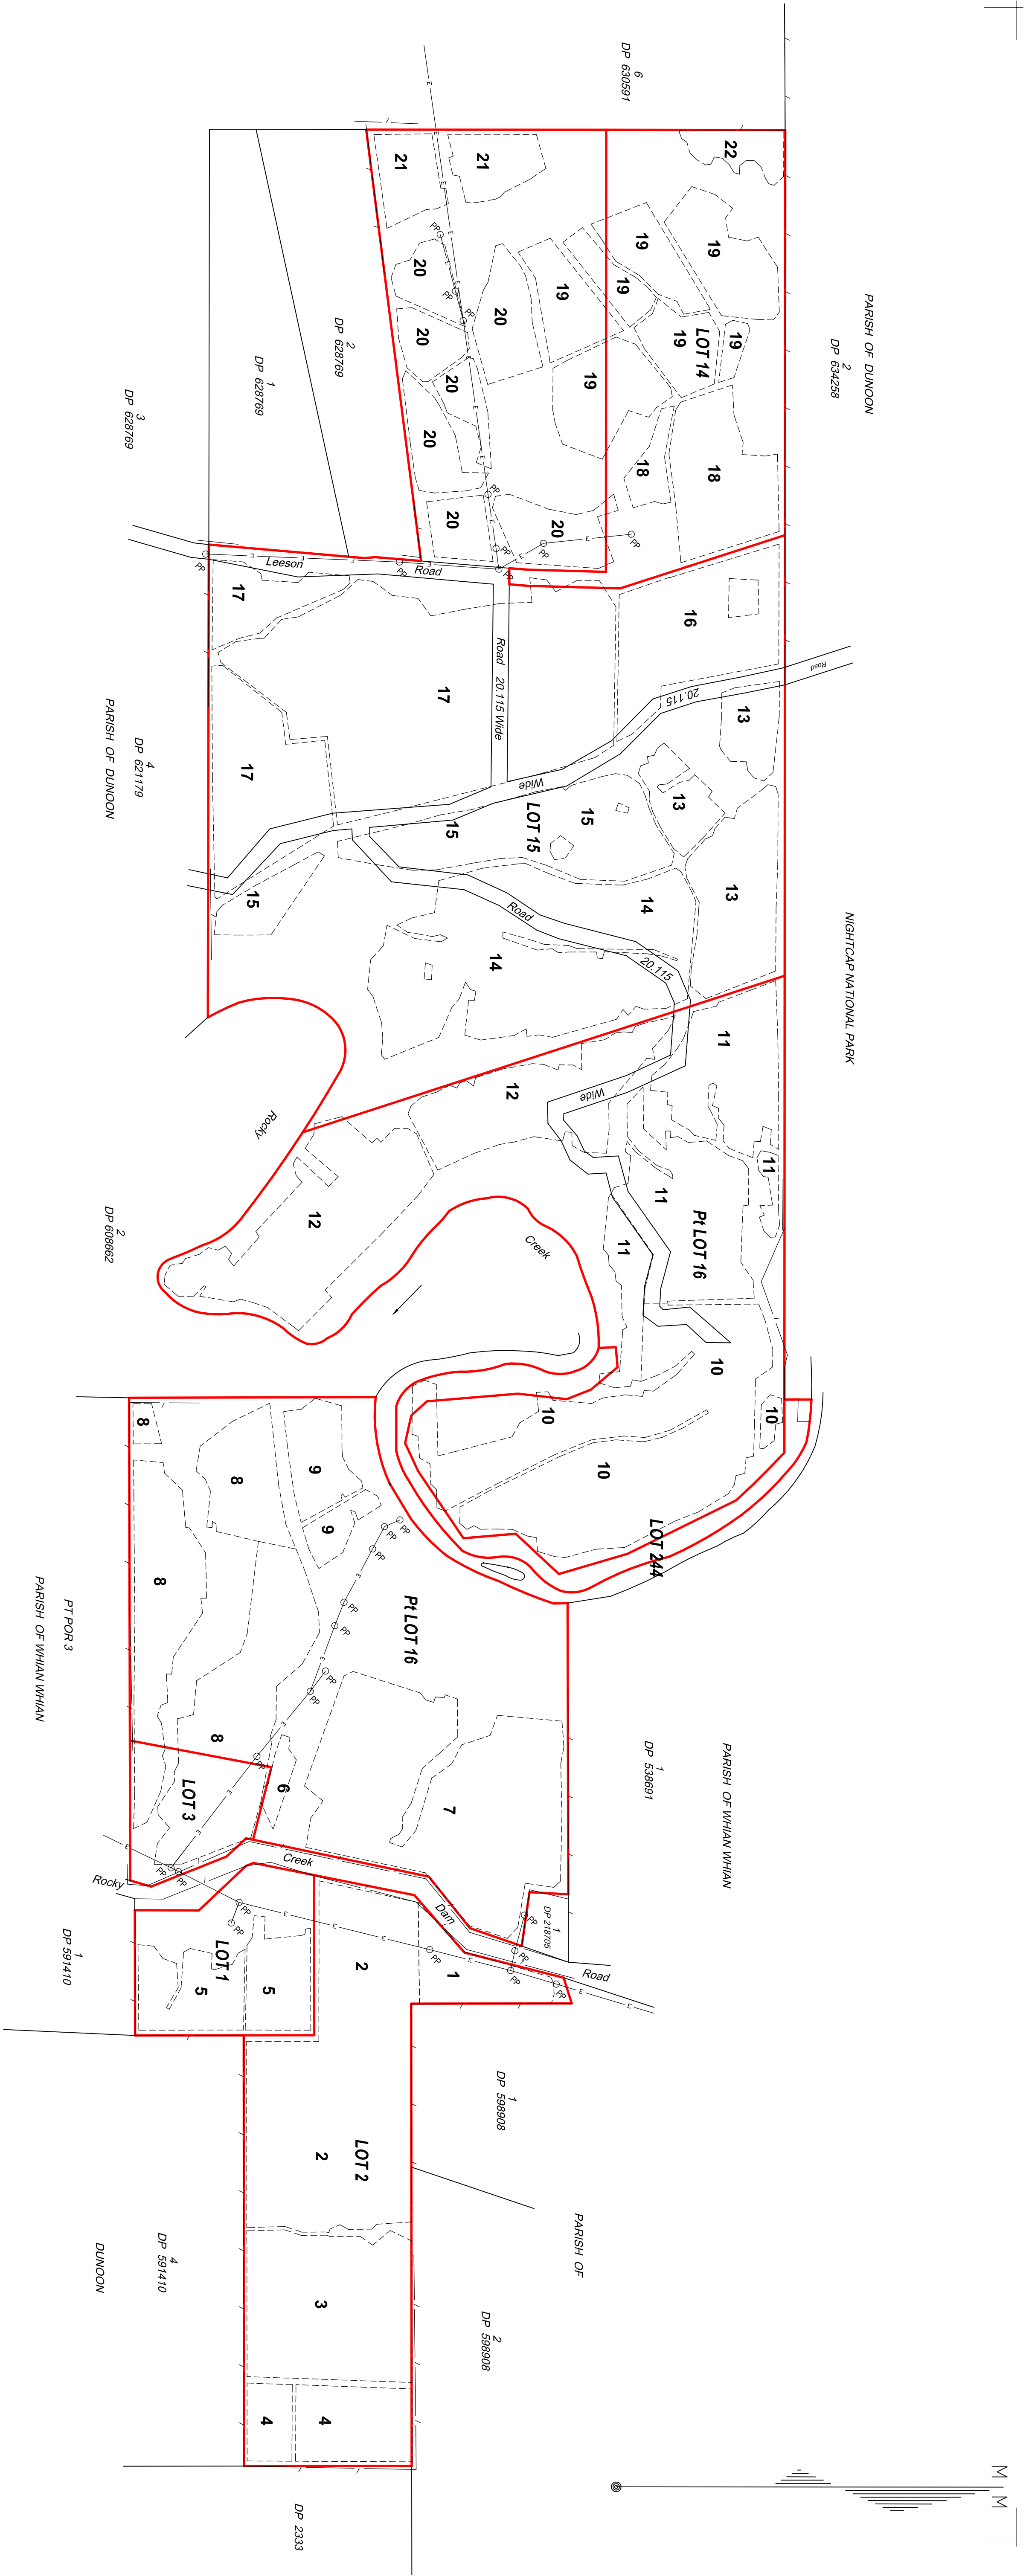

LEGEND


BOUNDARY

TREE AREA

FENCE LINE

OVERHEAD POWER LINES

LOT 14	DP827766	12.19ha	
LOT 15	DP827766	52.72ha Excluding Road,	
LOT 16	DP827766	53.14ha Excluding Road,	Road Reserve Within Lot 15 Adj 3.9ha
LOT 244	DP725894	2.352ha	Road Reserve Within Lot 16 Adj 1.3ha
LOT 3	DP632934	2.299ha	
LOT 2	DP555501	14.59ha	
LOT 1	DP555501	4.047ha	
TOTAL LOT AREA		141.3ha Excluding Roads	
		146.5ha Including Roads	

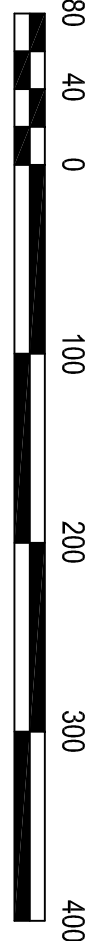

SCALE 1:4000 AT A1

Year	Planted	Block	Area ha	Tree Spacing	Row	Variety	Count
1980	1	1.07	3	7	7	246.800.344	450
1980	2	6.99	3	7	7	246.800.344	2694
1984	3	3.68	3	7	7	246.333.503.344	1552
1985	4	1.87	3	7	7	246.344	783
1986	5	2.14	3.5	7	7	246.344	793
1985	6	0.24	3.5	6	6	246.508.344	208
1985	7	6.64	3	7	7	246.508.344	3116
1986	8	3.76	3	7	7	246.508.344	799
1986	8	0.14	5	7	7	246.508.344	148
1986	8	2.44	5.5	7	7	246.508.344	665
1986	8	1.35	6	7	7	246.508.344	585
1986	9	1.37	5.5	7	7	246.344	385
1987	10	7.62	3	7	7	246.508.333.344	3225
1988	11	5.78	3	7	7	246.508.333.344	2428
1988	11	0.18	3.5	7	7	246.508.333.344	83
1989	12	6.35	3.5	7	7	246.508.333.344	2313
1990	13	3.68	3.5	7	7	246.508.333.344	1593
1991	14	6.76	3.5	7	7	246.800.344	2646
1991	15	3.73	3.5	7	7	246.800.344	1426
1993	16	2.80	3.5	7	7	246.800.344.741.OV	1101
1995	17	13.64	3.5	7	7	246.800.344.741.OV.A4.849.A38	5277
1996	18	2.47	3.5	7	7	246.800.344.741.OV.A4.A16.A38	1266
1998	19	5.96	3.5	7	7	A203.849.246.A199	2523
1998	20	4.74	3.5	7	7	A203.A268.815.781.842.816.849.DAD.A4.A16.V47	1325
1995	21	1.53	3.5	7	7	Daddo's	658
2011	22	0.55	5	10	10	Daddo's	98
	Total	97.47					38130

LOCALITY: DUNOON
LGA: LISMORE
CAOFILE:LM090092-SV11
CIVIL:CAOFILE:LM090092-CO8

SCALE 1:4000 (A1)



LandPartners Limited
24 Carrington Street, Lismore
NSW 2460, Australia
Phone: (02) 6627 9500 Fax: (02) 6621 7854
www.landpartners.com.au

Surveyed: LM Date Surveyed: JULY2011
Drawn: G.C Checked:

Dwg. No.
LM090092-SV11